Etude Capacitaire

LOCALISATION 156B-158-158B AV RAYMOND BARRE - 97427 L ETANG SALE
DATE 30/09/2026

AVANT PROPOS

L'étude a été réalisée sur la base d'extrait du PLU d'ETANG SALE du 22 JUIN 2017 - Modifié le 4 décembre 2024

Informations complémentaires

MIXITE FONCTIONNELLE ET SOCIALE: Tout projet visant à créer plus de 1 000 m² de surface de plancher destinée à l'habitation doit prévoir
d'affecter au logement aidé au moins 20% de la surface de plancher d'habitation prévue dans l'opération.

PLS et LLI (80% de T2 et 20% de T3)
Ou 100% de T2.

DONNEES

Nature de l'opération	Construction de logements collectifs
Références cadastrales	000AW99 (501) - AW451 (586) - AW 624 (274) -AW625 (385)
Surface de l'assiette foncière du projet (m²)	1746
Zones du PLU	UA
Implantation	VOIES ET EMPRISES PUBLIQUES:en retrait de l'alignement, avec un recul minimum de 4,00m LIMITES SEPARATIVES: sur une ou deux limites avec linéaire =15m pour hab et 20m pour commerce, Si retrait >3m (hors balcons sur 1m et protection solaire)
Constructions sur le même	3m
Emprise au sol (CES)	70%
Surface de plancher	
Epannelage	12m égout - 15m faitage - 13m acrotère
Clôtures	Murs de soutènement: <3m sinon redan de 1m, Si pente >15% ht=4m ponctuellement
Stationnement	Planté 1 arbre pour 2 places et perméble à 50% 1 place jusqu'au T2 1,5 places jusqu'au T4 2 places pour T5 Cellule commerciale: 1 place si <100m²
Local 2 roues et poussettes	1m² jusqu'au T2 et 1,5m² au-delà
Espaces verts	20% espaces verts hors stationnement engazonnés- 1arbre pour 50m² EV Marge plantée 2m sur 75% du linéaire sauf mitoyenneté
Perméabilité	30%
Local OM	
Local Ménage	

ETUDE

PROPOSITION :

	SP m² y/c coursives et varangues	SU (adm)m²	SHAB + varangue		Nb de logements T2	T3	T4	Totaux
Rez de Chaussée commercial	0	95	0	0				
Rez de Chaussée	635		452		7	1		8
R+1	730		515		7	2		9
R+2	726		515		7	2		9
R+3	277		171		2	1		3
TOTAL	**2 368**	**95**	**1 653**		**23**	**6**	**0**	29
				%	79%	21%	0%	100%
				soit	**29**	**logements**		
Pourcentage de logements sociaux réglementaires			20%	**dont**	**5,8**	**sociaux**		

	Réglementaire		Projet		
Emprise au sol	1222.20	m²		m²	
Perméabilité	523.80		710.00		
Stationnement	30	places	31	places	dont une place pour le comr
Local vélos	32.00	m²	32.00	m²	
SHOB Parking			670.00	m²	

OCEANIS

30 rue de la Clinique
97490 Ste Clotilde

Construction de logements

156 Avenue Raymond Barre 97427 ETANG SALE



PHASE

Etude capacitaire

01 Plan de situation
02 Plan de masse
03 Plan des niveaux sous-sol et RDC
03 Plan des niveaux 1 à 3
04 Plan type T2 et coupe gabarit
05 Intentions Architecturales


26024	CG	FORMAT A3	DATE 14/10/2026	INDICE B


ARCHITECTE:

i ARCHITECTES
4, Rue Camille Franck Cadet
97427 L'étang-Salé
Tel: 02 97 30 57 90
contact@iarchitectes.com



Parcelles faisant l'objet du présent projet :
000AW99 (501) - AW451 (586) - AW 624 (274) - AW625 (385)
Surface cadastral : 1746M²
Adresse : 156B-158-158B AV RAYMOND BARRE - 97427 L ETANG SALE

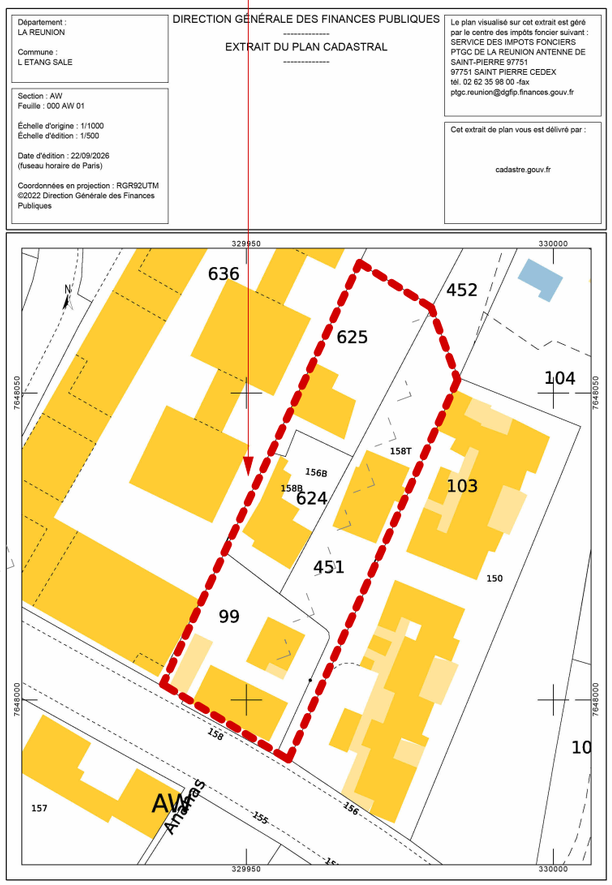

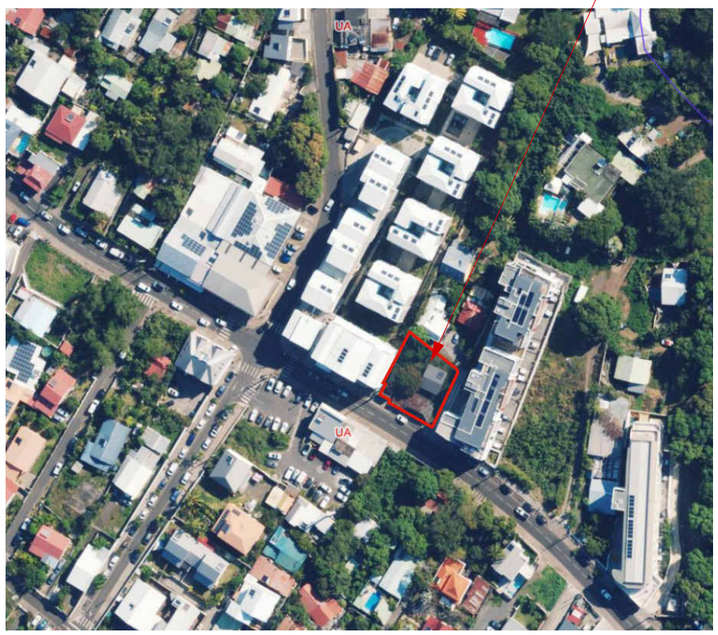

Plan de cadastre
Echelle : 1 : 1000

MAITRISE D'OUVRAGE :
OCEANIS

ADRESSE DU PROJET :
156 Avenue Raymond Barre 97427 ETANG SALE

Plan de situation

REFERENCE :	PHASE :	INDICE :
26024	CAPA	B

ECHELLE :	DATE :	AUTEUR :	N° PIECE :
1 : 1000	14/10/2026	CG	01

ARCHITECTES



29 logements comprenant
10 T2 et 13 T2 bis
6 T3 SOCIAUX
1 commerce de 98m²
31 parkings dont 1 aérien

R+3

SP compris coursives et varangues = 2 368m²
+ 95m² se SU de l'espace commercial
SHAB VARANGUES = 1 653M²

Plan masse
Echelle : 1 : 500

MAITRISE D'OUVRAGE :
OCEANIS

ADRESSE DU PROJET :
156 Avenue Raymond Barre 97427 ETANG SALE

Plan de masse

REFERENCE :	PHASE :	INDICE :
26024	CAPA	B


ECHELLE :	DATE :	AUTEUR :	N° PIECE :
1 : 500	14/10/2026	CG	02

ARCHITECTES



Niveau -1

Echelle : 1 : 500

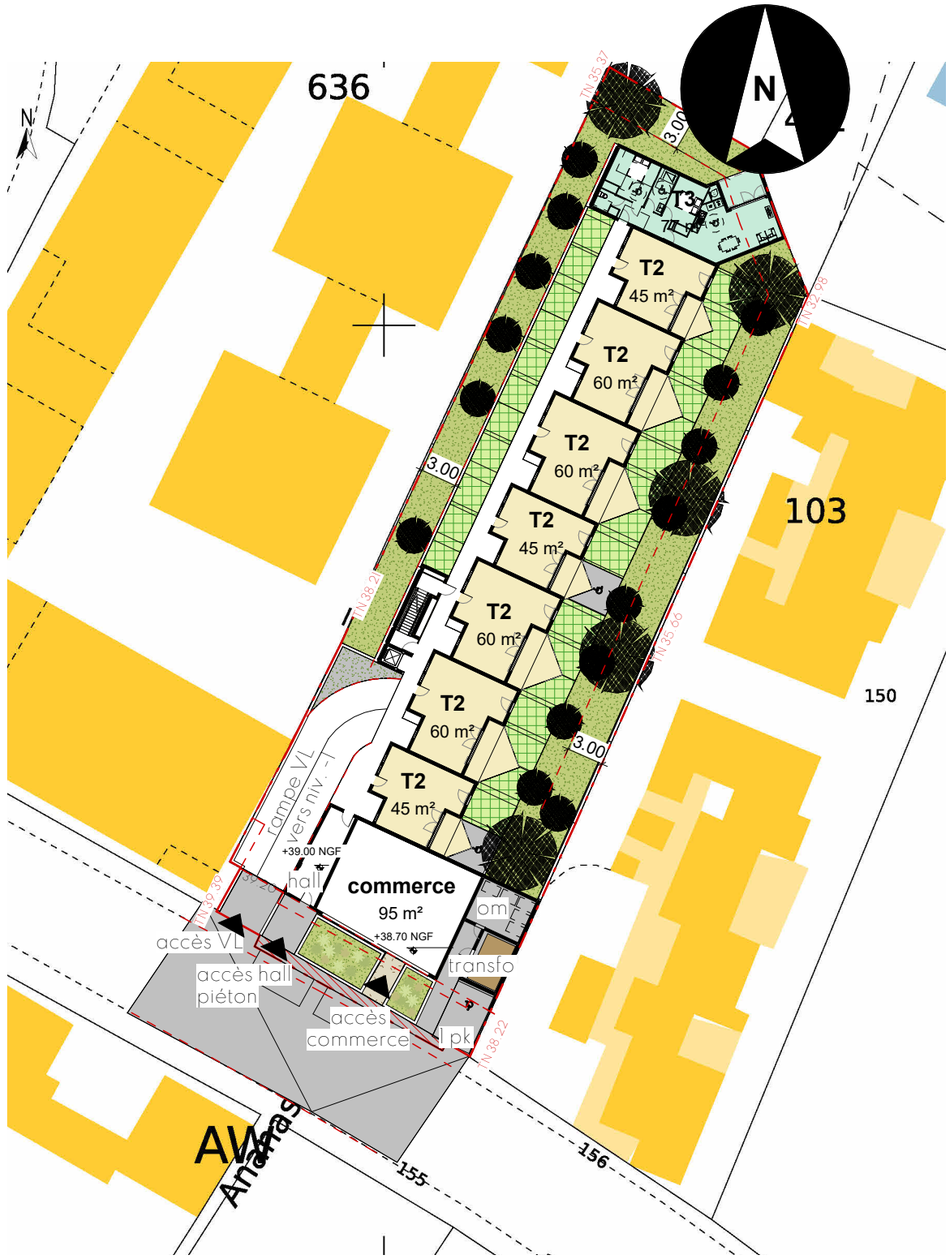

Niveau 0 - sur rue

Echelle : 1 : 500

MAÎTRISE D'OUVRAGE :

OCEANIS

ADRESSE DU PROJET :


156 Avenue Raymond Barre 97427 ETANG SALE


Plan des niveaux sous-sol et RDC

REFERENCE :	PHASE :	INDICE :
26024	CAPA	B

ECHELLE :	DATE :	AUTEUR :	N° PIECE :
1 : 500	14/10/2026	CG	03

ARCHITECTES

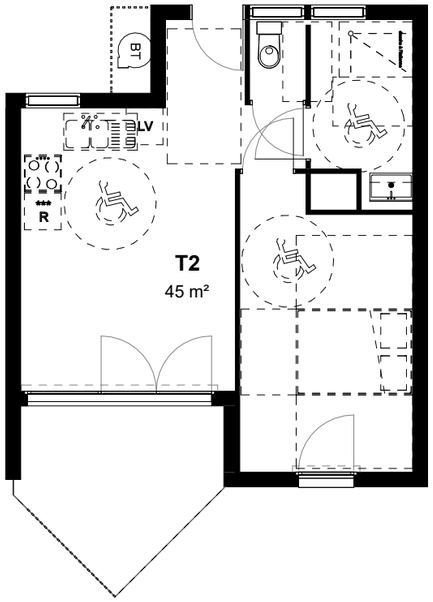

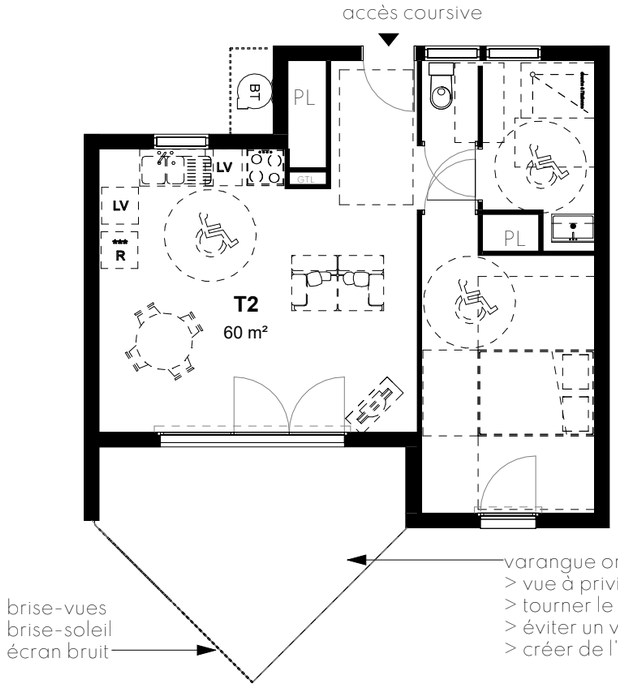

Plan type T2BIS

Echelle : 1 : 100



Coupe 1

Echelle : 1 : 200

MAITRISE D'OUVRAGE :

OCEANIS

ADRESSE DU PROJET :

156 Avenue Raymond Barre 97427 ETANG SALE

Plan type T2 et coupe gabarit

REFERENCE :	PHASE :	INDICE :
26024	CAPA	B

ECHELLE :	DATE :	AUTEUR :	N° PIECE :
Comme indiqué	14/10/2026	CG	04

ARCHITECTES



MAITRISE D'OUVRAGE :

OCEANIS

ADRESSE DU PROJET :

156 Avenue Raymond Barre 97427 ETANG SALE

Intentions Architecturales

REFERENCE :	PHASE :	INDICE :
26024	**CAPA**	**B**

ECHELLE :	DATE :	AUTEUR :	N° PIECE :
	14/10/2026	CG	05

ARCHITECTES