OCEANIS PROMOTION

"Le QG" 30 rue de la Clinique
97490 Ste Clotilde

Construction de MIG

50-66 rue leconte Delisle 97416 ST LEU

PHASE

Etude CAPACITAIRE


01 Plan de situation et de cadastre
02 Plan masse parcelle AC 261
03 Plan masse parcelle AC 264
03 Plans type logements

25023	CG	FORMAT	A3	DATE	**02/06/2026**	INDICE	**2**

ARCHITECTE:


i ARCHITECTES
4 rue Franck Camille Cadet
97427 ETANG SALE
Tel:02 93 86 47 57
contact@iarchitectes.com

Parcelles faisant l'objet du présent projet : AC 261 et AC 264
Surface cadastral : 12 261m² - 9 979m²
Adresse : 50-66 rue leconte Delisle 97416 ST LEU
Zonage PLU: Ud

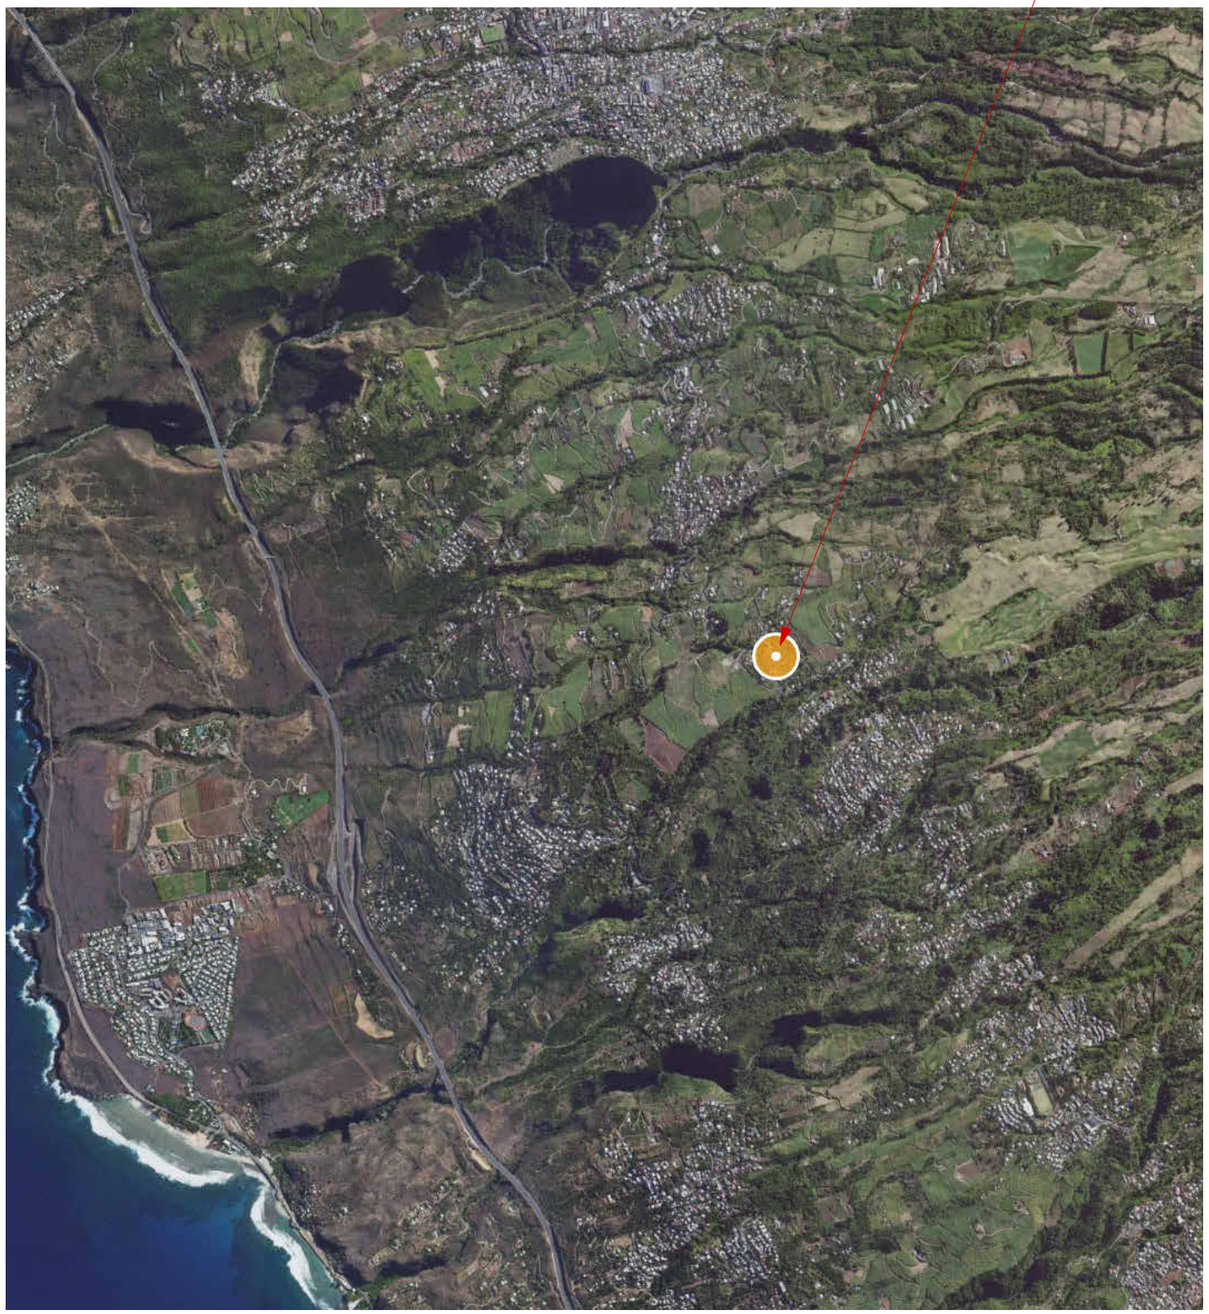

Plan de situation

Echelle : 1 : 5000

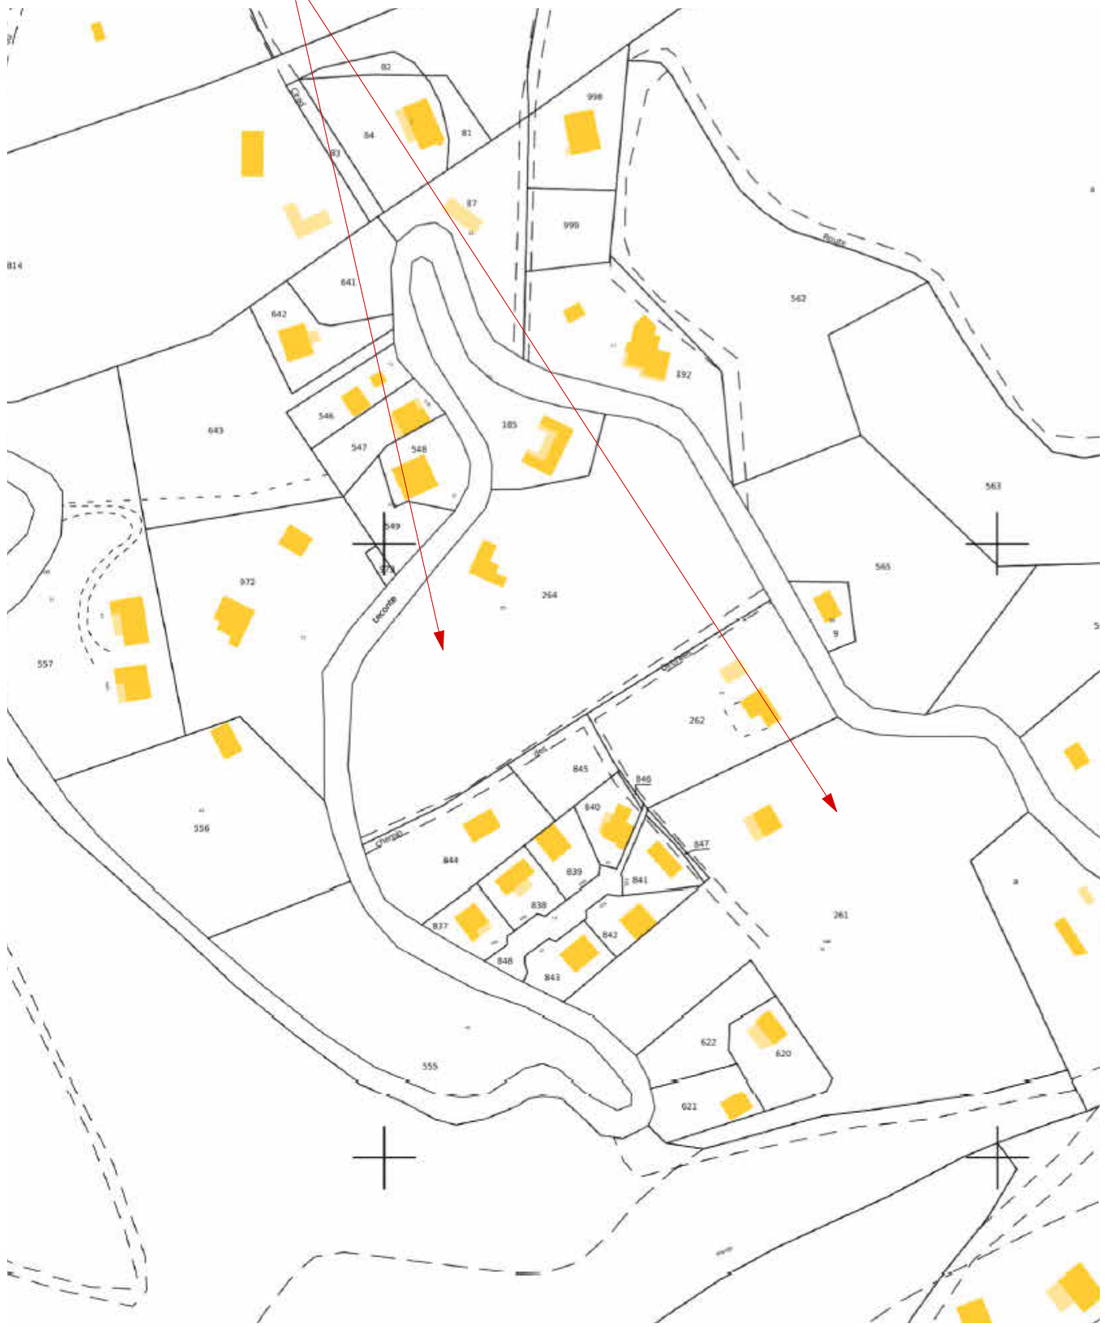

Plan de cadastre

Echelle : 1 : 2000

MAITRISE D'OUVRAGE :

OCEANIS PROMOTION

ADRESSE DU PROJET :

50-66 rue leconte Delisle 97416 ST LEU

Plan de situation et de cadastre

REFERENCE :	PHASE :	INDICE :
25023	**CAPA**	2

ECHELLE :	DATE :	AUTEUR :	N° PIECE :
Comme indiqué	02/06/2026	CG	01

ARCHITECTES



Sol: Cheminement piéton sur terre plein	751.70 m²
Sol: pavés à joints enherbés	1197.78 m²
Sol: Pleine Terre commun	2391.98 m²
Sol: Pleine Terre privatif	7011.61 m²
Sol: Voirie principale	1609.84 m²
Sol: Voirie secondaire	814.26 m²

MAITRISE D'OUVRAGE :

OCEANIS PROMOTION

ADRESSE DU PROJET :

50-66 rue leconte Delisle 97416 ST LEU

Plan masse parcelle AC 261

REFERENCE : 25023

PHASE : **CAPA**

INDICE : 2


ECHELLE : 1 : 500

DATE : 02/06/2026

AUTEUR : CG

N° PIECE : 02

ARCHITECTES

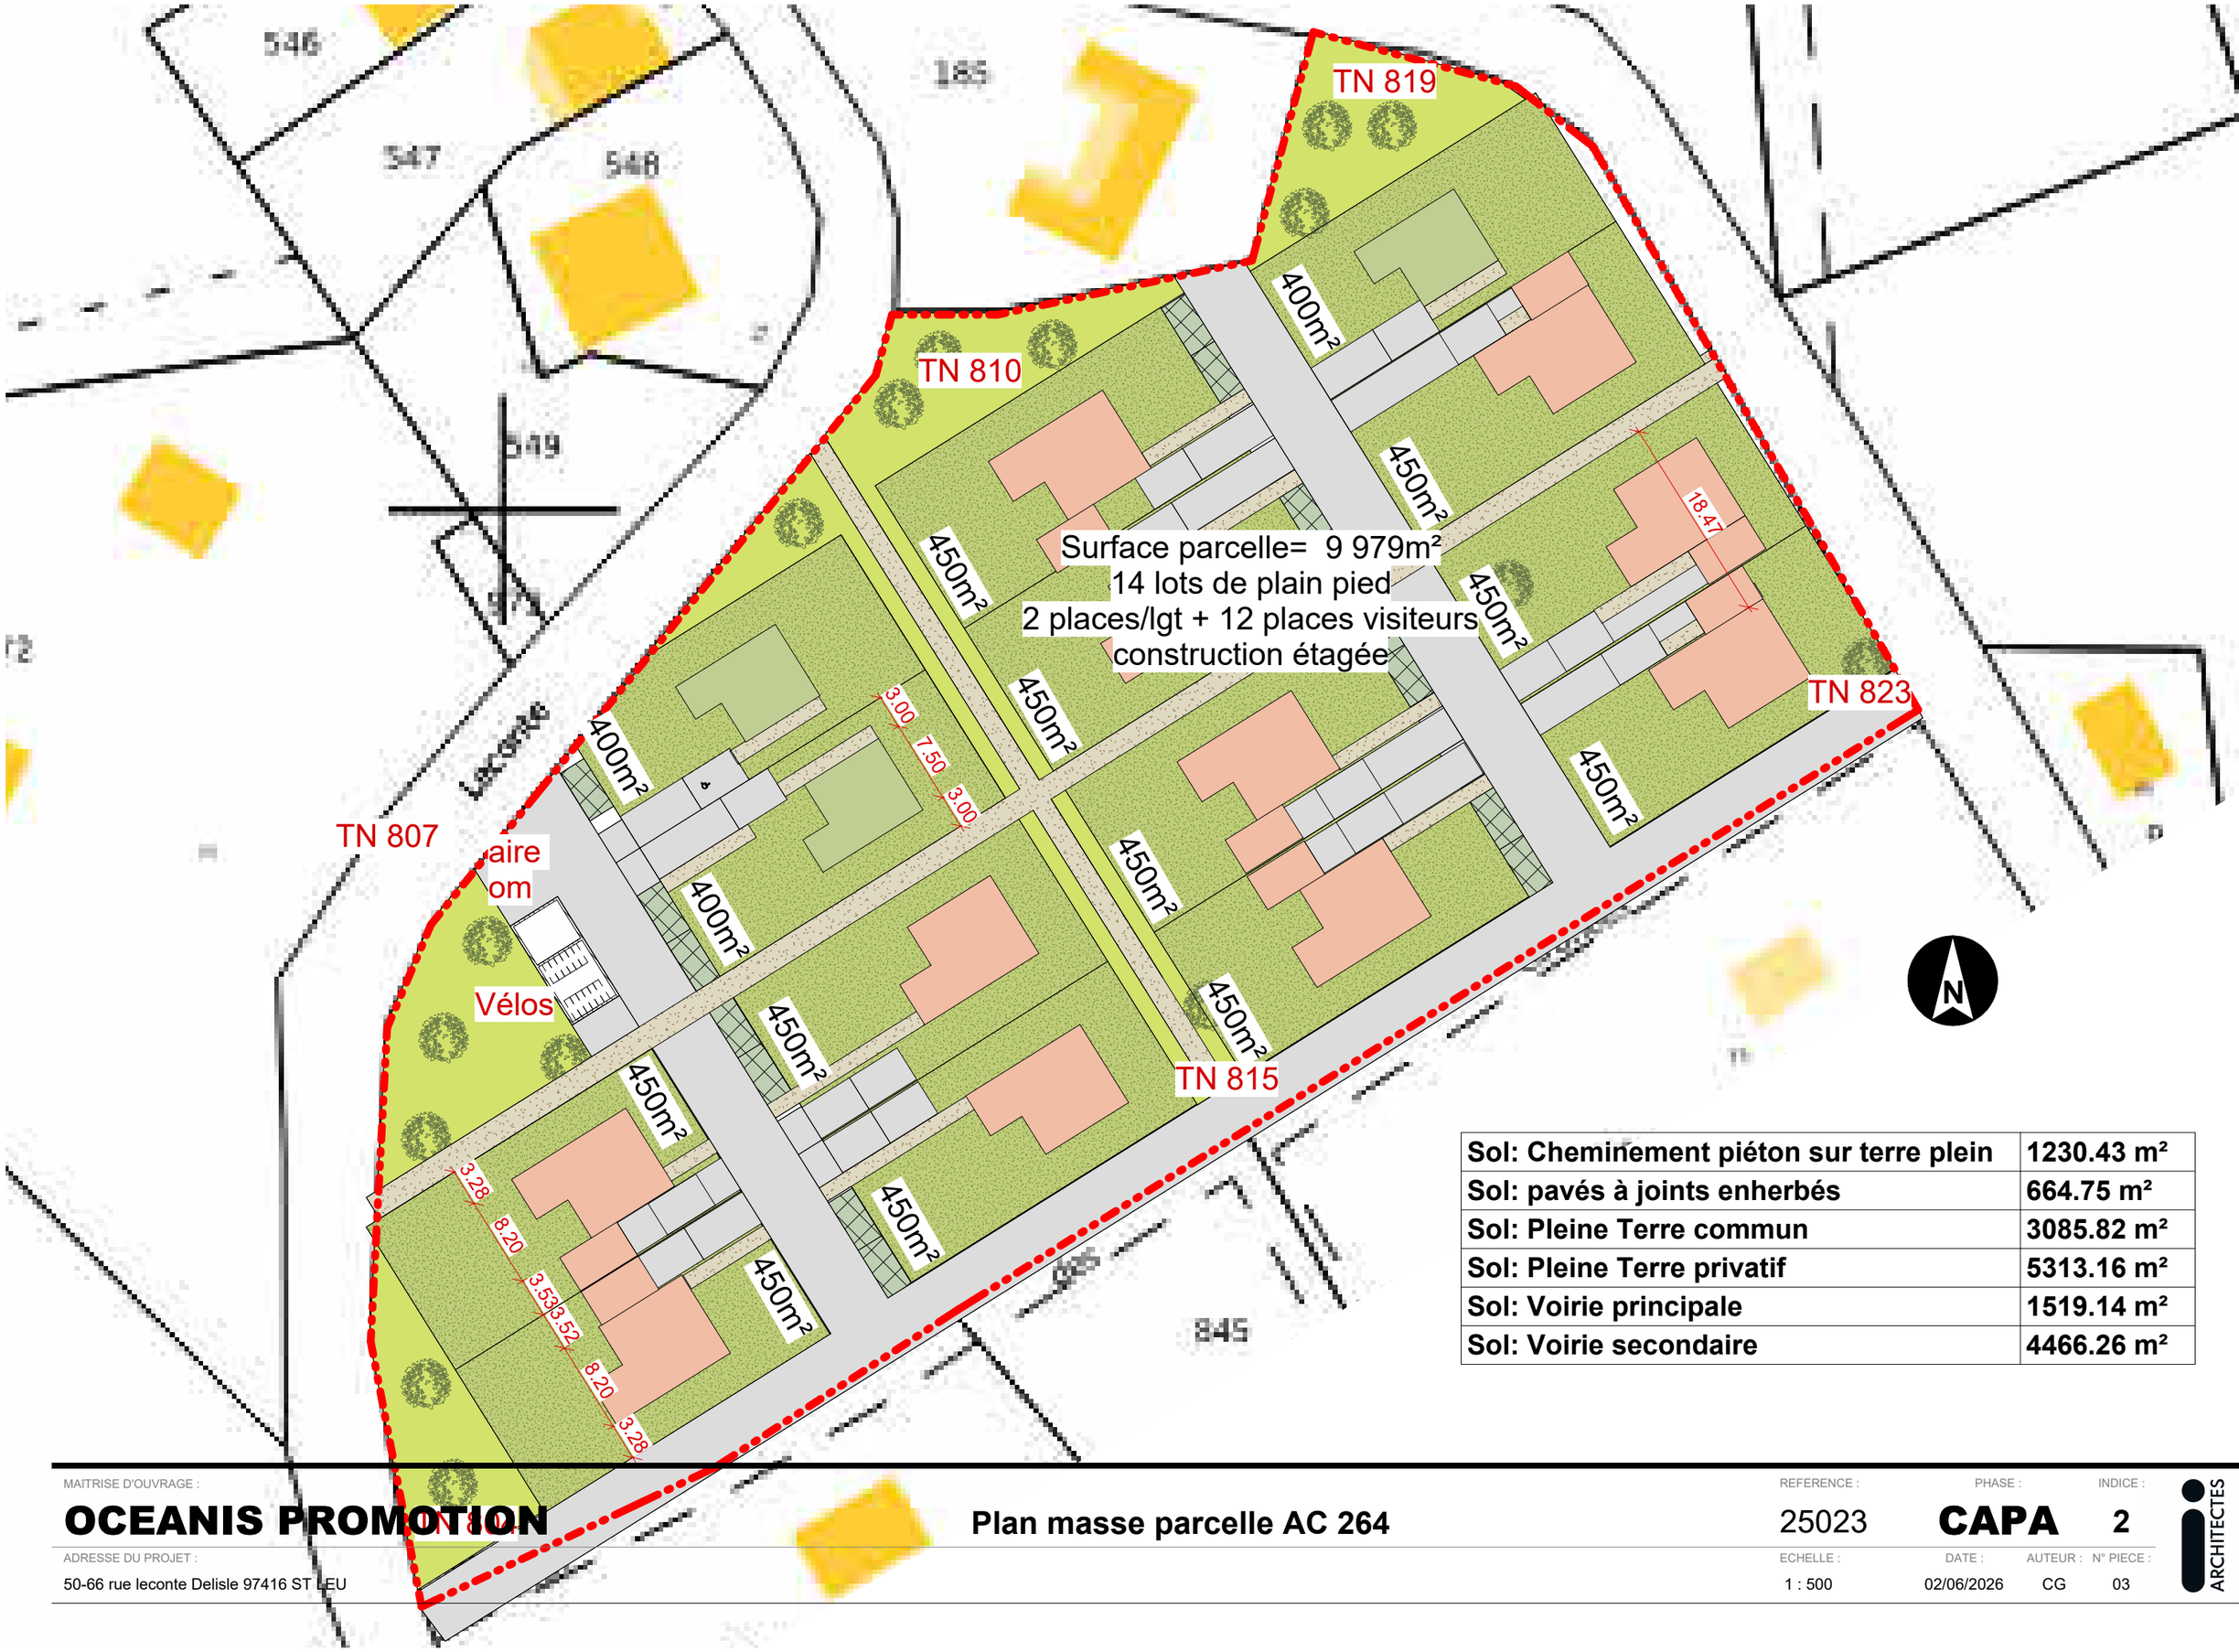

Sol: Cheminement piéton sur terre plein	**1230.43 m²**
Sol: pavés à joints enherbés	**664.75 m²**
Sol: Pleine Terre commun	**3085.82 m²**
Sol: Pleine Terre privatif	**5313.16 m²**
Sol: Voirie principale	**1519.14 m²**
Sol: Voirie secondaire	**4466.26 m²**

MAITRISE D'OUVRAGE :

OCEANIS PROMOTION

ADRESSE DU PROJET :

50-66 rue leconte Delisle 97416 ST LEU

Plan masse parcelle AC 264

REFERENCE : 25023

PHASE : **CAPA**

INDICE : 2


ECHELLE : 1 : 500

DATE : 02/06/2026

AUTEUR : CG


N° PIECE : 03

ARCHITECTES

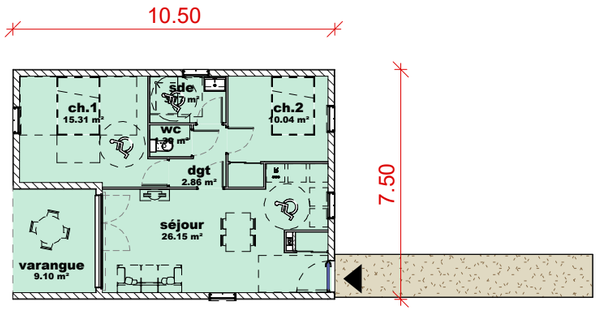


T3a

ch.2	10.04 m²
séjour	26.15 m²
sde	3.77 m²
ch.1	15.31 m²
wc	1.39 m²
dgt	2.86 m²
varangue	9.10 m²
	68.63 m²

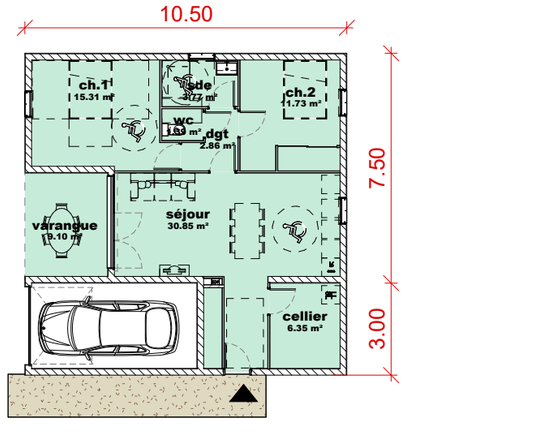


T3b

ch.2	11.73 m²
séjour	30.85 m²
sde	3.77 m²
ch.1	15.31 m²
wc	1.39 m²
dgt	2.86 m²
varangue	9.10 m²
cellier	6.35 m²
	81.38 m²

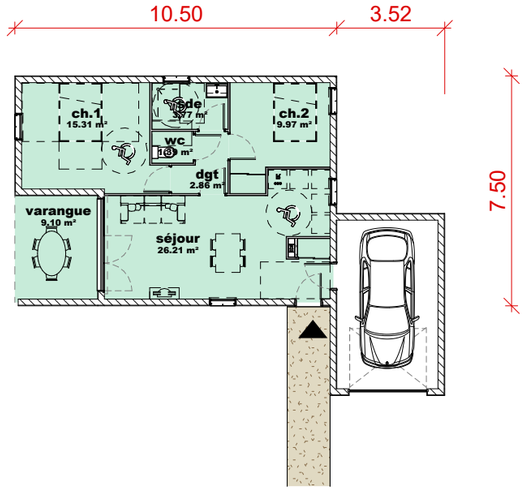


T3c

ch.2	9.97 m²
séjour	26.21 m²
sde	3.77 m²
ch.1	15.31 m²
wc	1.39 m²
dgt	2.86 m²
varangue	9.10 m²
	68.62 m²

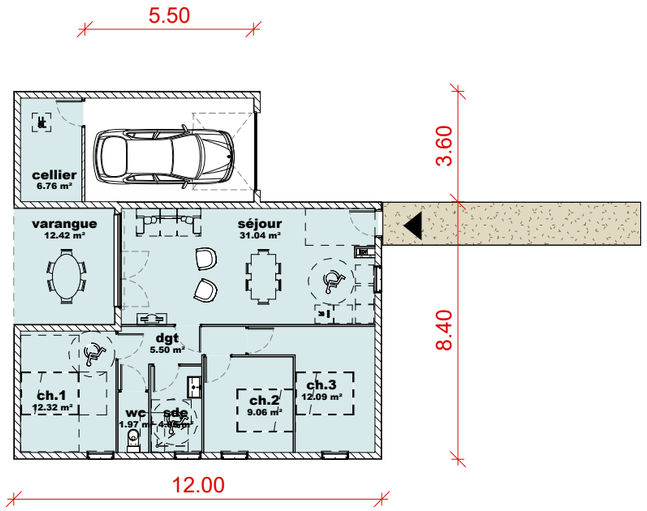

T4a

ch.1	12.32 m²
ch.2	9.06 m²
ch.3	12.09 m²
sde	4.66 m²
wc	1.97 m²
dgt	5.50 m²
séjour	31.04 m²
cellier	6.76 m²
varangue	12.42 m²
	95.82 m²

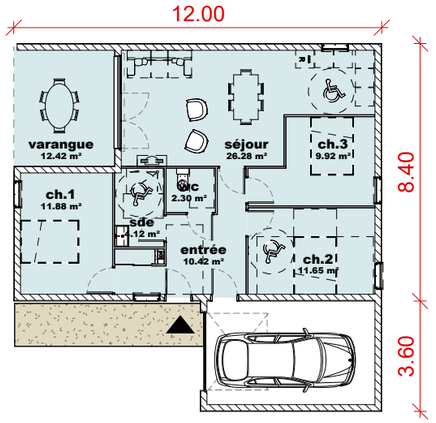

T4b

ch.1	11.88 m²
entrée	10.42 m²
ch.2	11.65 m²
séjour	26.28 m²
ch.3	9.92 m²
sde	4.12 m²
wc	2.30 m²
varangue	12.42 m²
	89.00 m²

MAITRISE D'OUVRAGE :

OCEANIS PROMOTION

ADRESSE DU PROJET :

50-66 rue leconte Delisle 97416 ST LEU

Plans type logements

REFERENCE : 25023

PHASE : **CAPA**

INDICE : 2

ECHELLE : 1 : 200

DATE : 02/06/2026

AUTEUR : CG

N° PIECE : 03

ARCHITECTES