Étude de faisabilité — · parcelles AW 99, 451, 624, 625

1 746 m² · zone UA · logement social · stationnement sous-sol 1 niveau

Votre projet — logement social : 40 logements demandés (30 T1 · 10 T2), stationnement sous-sol 1 niveau. Dépassement : au mieux 30 des 40 logements demandés tiennent sur ce terrain. Maximum réglementaire du terrain : 30 logements.

Ce qui limite : stationnement en sous-sol.

CONTRÔLES AUTOMATISÉS DE VOTRE PROJET
9 réussis · 0 échoués · 1 non effectués

STATUT DE L'ÉTUDE
Exploitable — à faire confirmer par un architecte

	Forme	Logements	Niveaux	Places	Étude
Votre projet	barre	30	R+1	30	Exploitable
Maximum du terrain	barre	30	R+1	30	indépendant de la demande

« Votre projet » = le programme que vous avez étudié ; « maximum du terrain » = le plus grand programme possible, indépendant de votre demande. Ce document n'affirme aucune conformité réglementaire.

1 746 m²
Contenance cadastrale

1 222 m²
Emprise au sol max

12 m
Hauteur (hauteur à l'égout)

6
Logements aidés imposés


30
Places imposées

1
Contrôles non effectués

Pré-faisabilité automatisée : scénarios indicatifs d'implantation établis à partir des règles publiées du PLU et des données publiques. Ce document n'est ni une étude d'architecte, ni une preuve de conformité, ni un dossier de permis.

1. Le terrain

4 parcelle(s), 1 746 m² au cadastre.

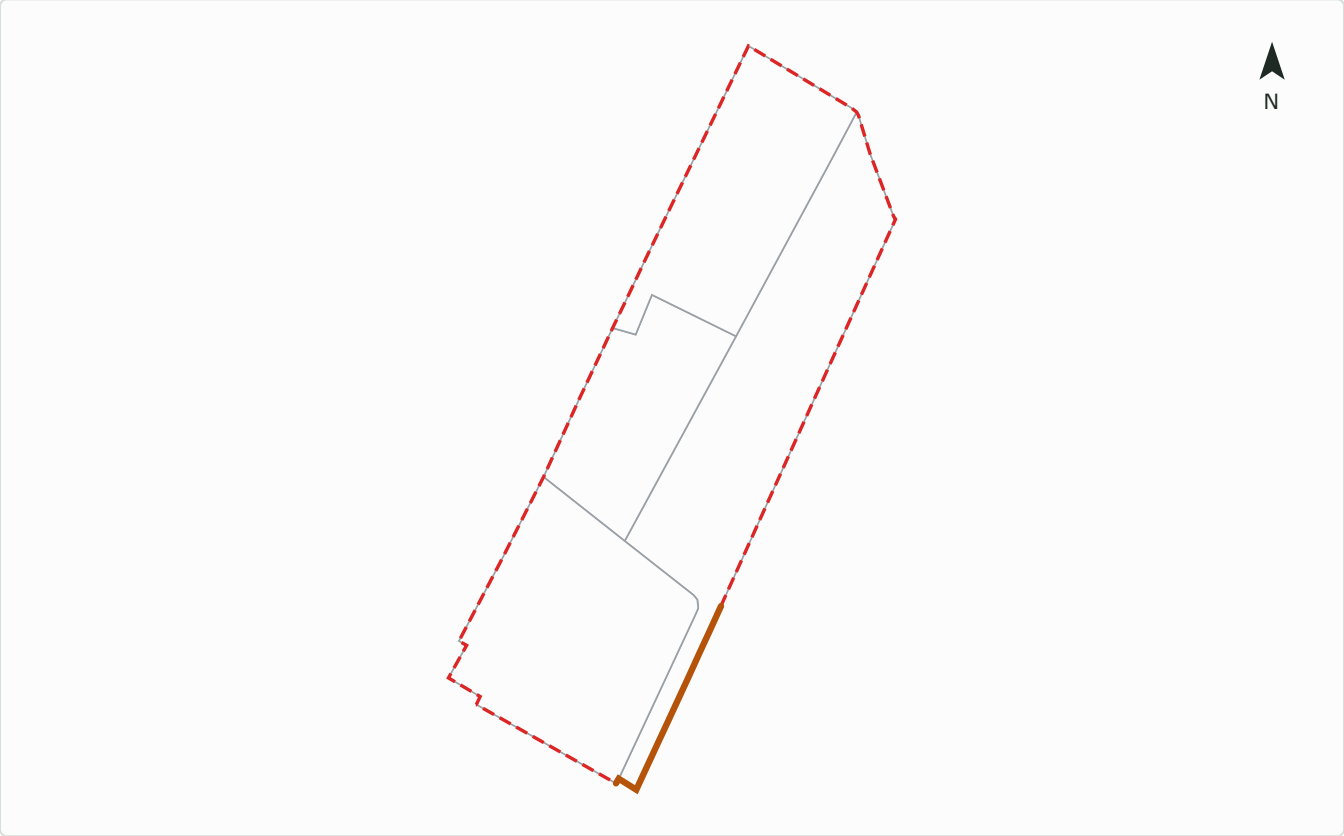

Parcelles Assiette Limite classée voie

Parcelle	Contenance	Nature
451	586 m²	Sourcé
624	274 m²	Sourcé
625	385 m²	Sourcé
99	501 m²	Sourcé
Assiette fusionnée	1 746 m²	

Terrain	Valeur	Nature
Pente moyenne	8 %	LiDAR HD

2. Règles et contraintes

Zone UA du PLU. Chaque valeur est citée ; une règle non validée reste « non effectuée », jamais tenue pour acquise.

Règle	Valeur	Nature
recul sur voie PLU · art. UA 2.1 · p. 17	4 m	Sourcé
recul sur limites séparatives PLU · art. UA 2.2 · p. 17	3 m	Sourcé
emprise au sol (CES) PLU · art. UA 2.4 · p. 18	70 %	Sourcé
hauteur à l'égout PLU · art. UA 2.5.2 · p. 19	12 m	Sourcé
hauteur au faîtage PLU · art. UA 2.5.2 · p. 19	15 m	Sourcé
pleine terre (perméabilité) PLU · art. UA 2.6 · p. 21	30 %	Sourcé
mixité sociale PLU · art. UA 1.3 (1) · p. 17	20 % · seuil 1 000 m²	Sourcé
stationnement (barème) PLU · art. UA 2.7.3 · p. 22	—	Sourcé

Aucune contrainte cartographiée ne touche le terrain.

Stationnement & mixité

Le PLU de L'Étang-Salé (art. UA 2.7.3) exige 1 pl. T1–T2 · 1,5 pl. T3–T4 · 2 pl. T5+.


La loi nationale (Code de l'urbanisme, art. L151-35) plafonne à 0,5 place/logt si le projet est éligible — à confirmer.

LABUSE a dessiné 30 places au sous-sol (niveau −1) selon la règle du PLU.

Mixité sociale (art. UA 1.3 (1)) : 20 % de logements aidés au-delà de 1 000 m² de SDP. Applicable : 6 logements aidés imposés.

3. Enveloppe constructible

Zone d'implantation de 1 155 m² après reculs et contraintes. Ce plafond n'est pas ce qu'on peut construire : c'est le scénario (plan masse) qui le dit.

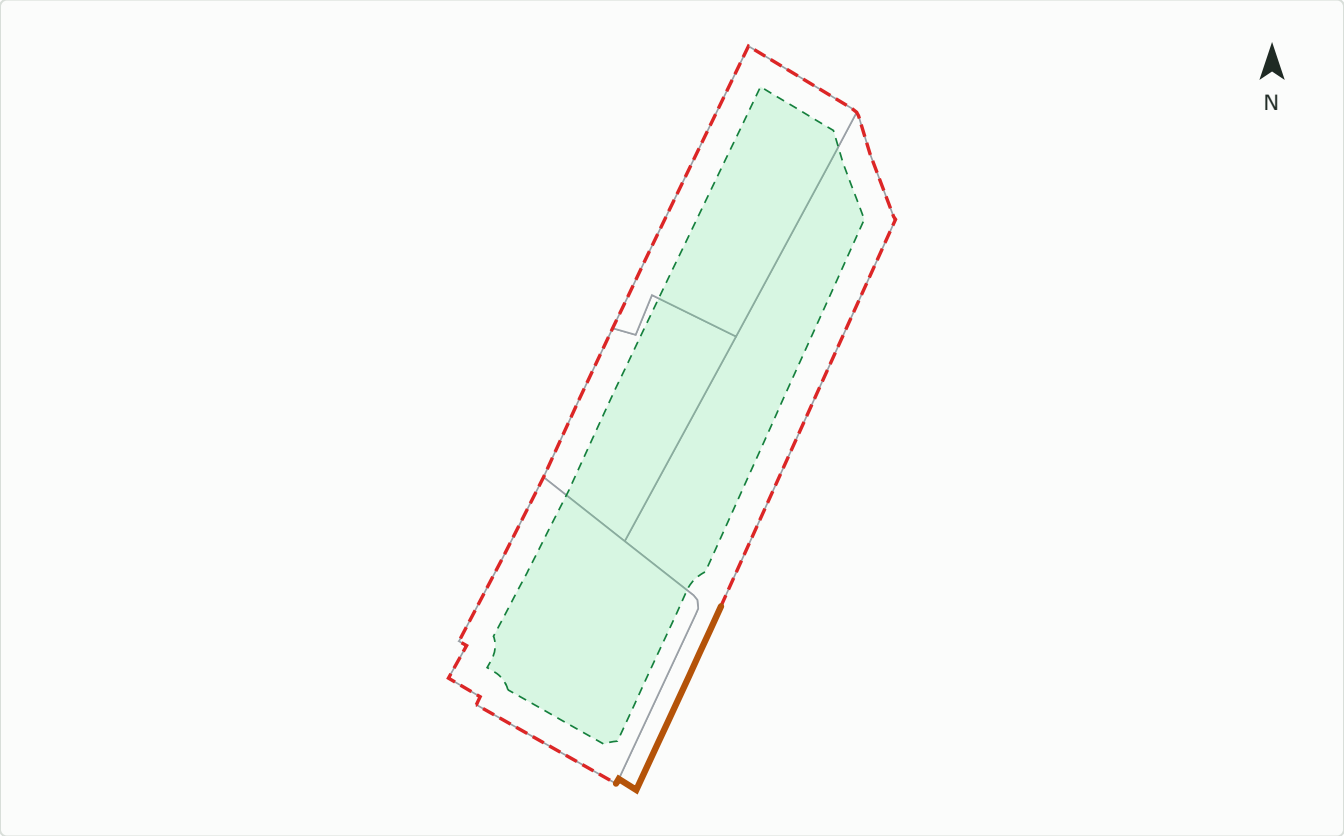


Parcelles · Assiette · Zone d'implantation · PPR rouge (retirée) · PPR bleue (signalée) · Limite classée voie

Surface	Valeur	Nature
Terrain (contenance)	**1 746 m²**	Sourcé
Zone d'implantation réglementaire	**1 155 m²**	ƒ Dérivé
Plafond d'emprise	**≤ 1222 m² (70 % de la contenance)**	ƒ Dérivé

4. Plan masse de votre projet

Scénario retenu — barre en R+1 : 30 logements, 30 places au sous-sol (niveau −1).

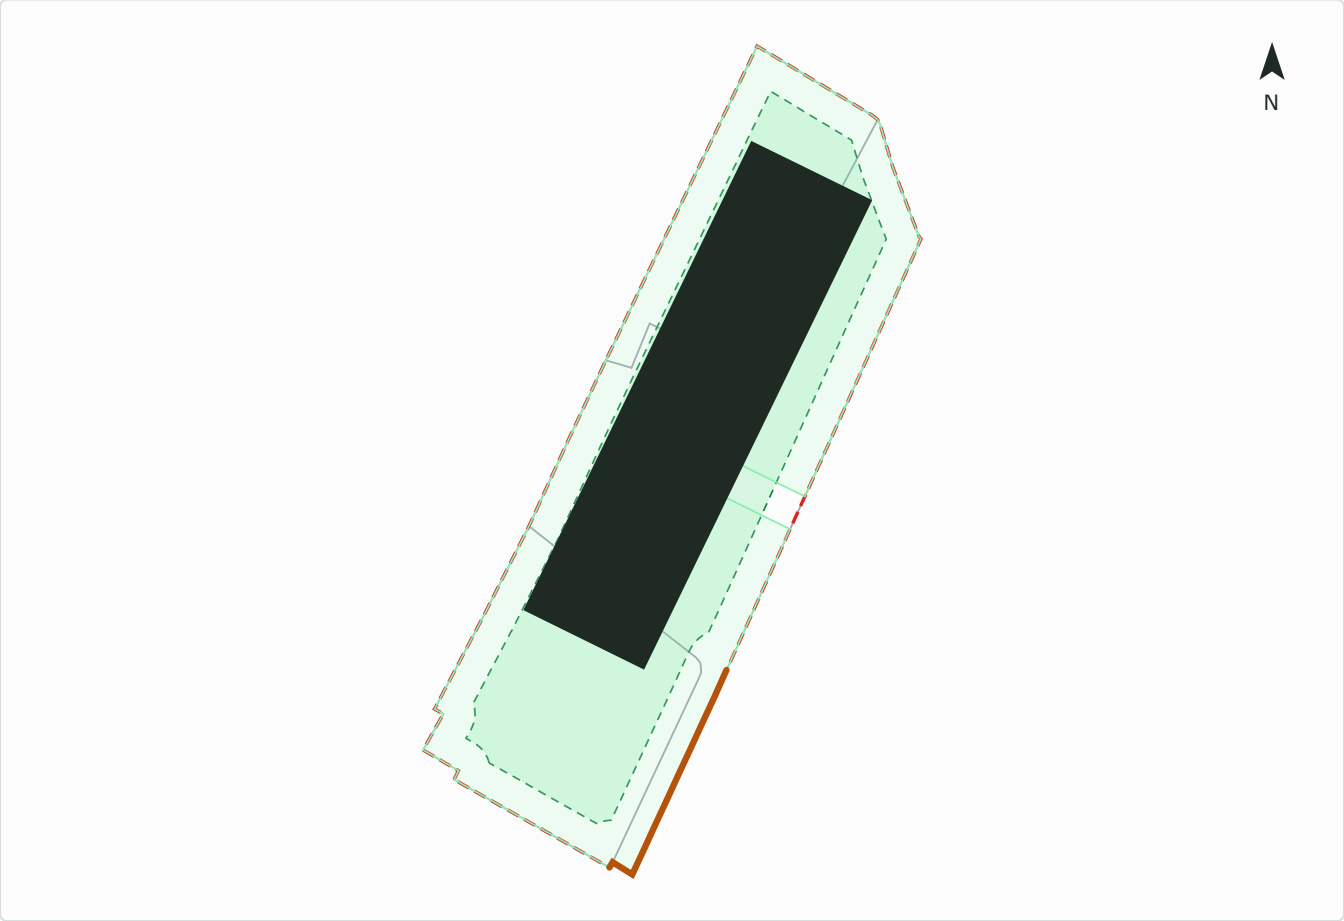

Bâtiment proposé · Places · Allée · Espaces libres · Accès · Zone d'implantation


Élément	Valeur	Nature
Emprise des bâtiments	659 m²	Estimé
Places dessinées	30	Estimé
Espaces libres · dont pleine terre	970 m²	ƒ Dérivé

Chaque nombre de ce tableau = nombre d'objets dans la géométrie (verrou de test). Plan rendu depuis la géométrie servie.


Stationnement en sous-sol — 1 niveau (30 places / niveau)

30 places au total · emprise enterrée 750 m² (≤ emprise réglementaire) · rampe 58 m². Plan de principe dessiné sur la géométrie réelle.

Niveau −1 — 30 places

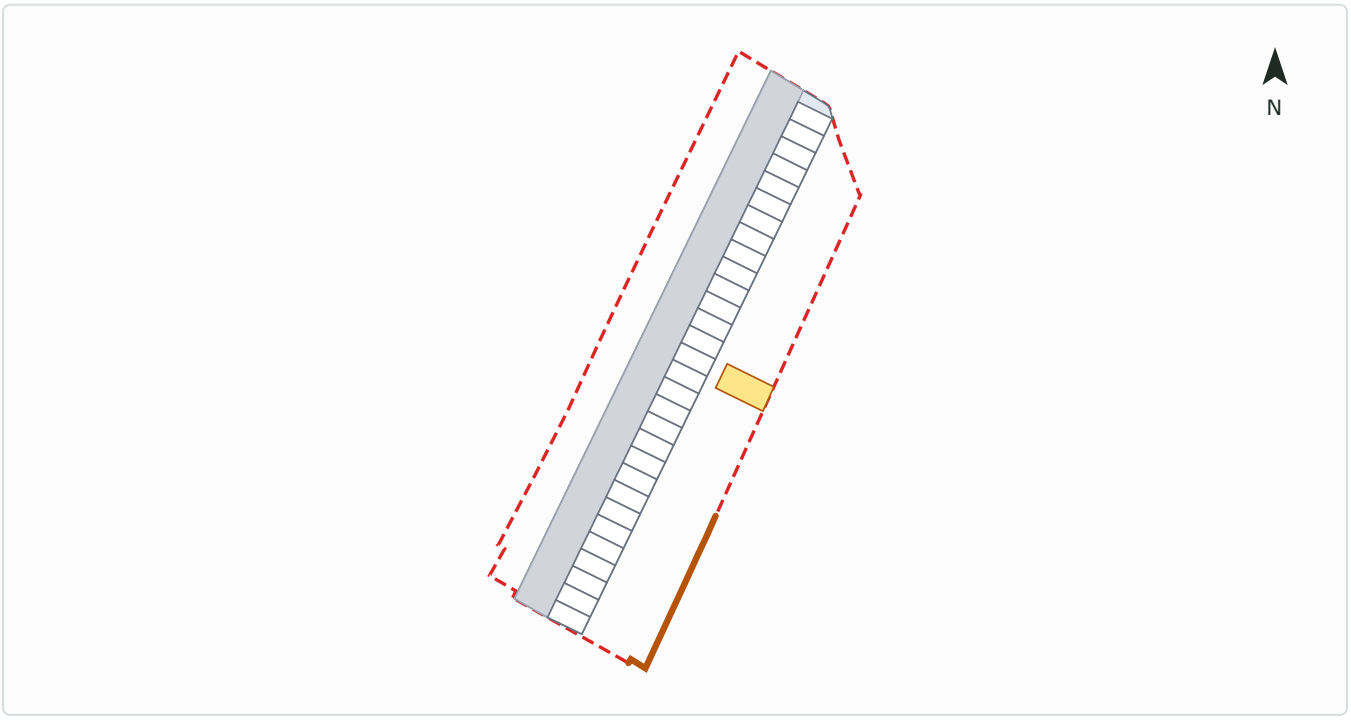

Emprise enterrée Places (−1) Allée (−1) Rampe d'accès

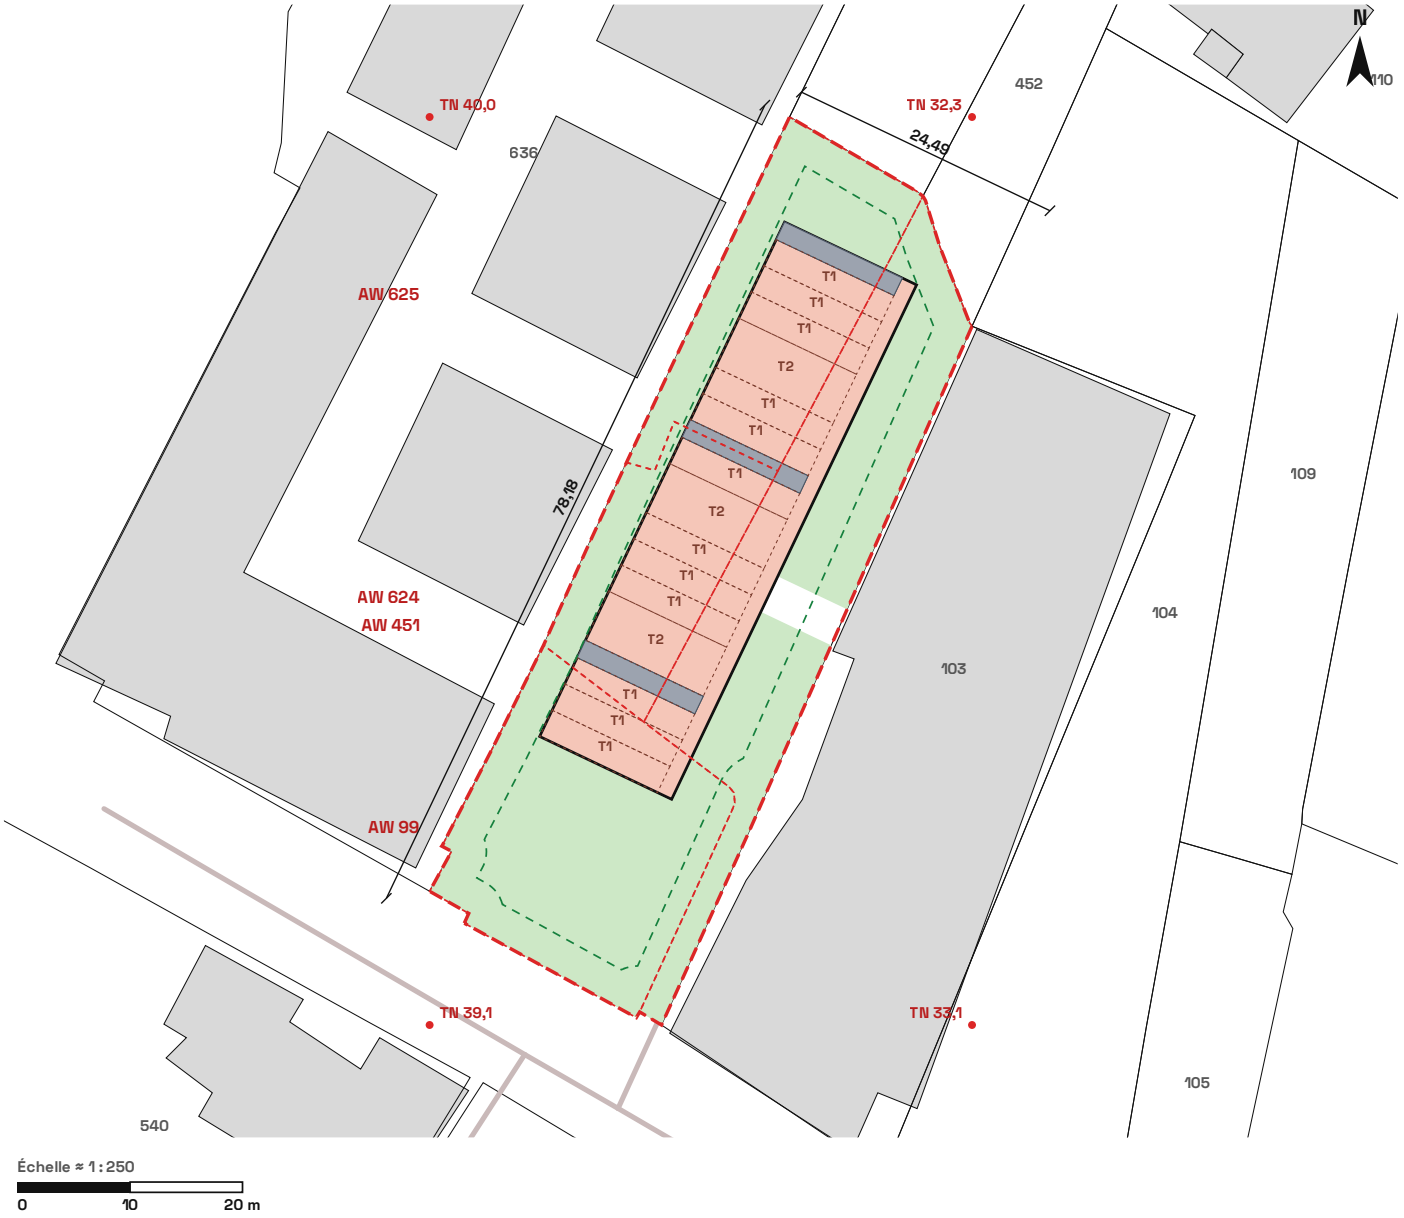

LÉGENDE

- Limite des parcelles étudiées
- Zone d'implantation réglementaire
- Bâtiment proposé
- Place de stationnement 2,50 × 5,00
- Allée, accès
- Espaces libres, pleine terre
- Bâti voisin (BD TOPO)
- PPR zone rouge (retirée)
- PPR zone bleue (signalée)

SURFACES (mesurées sur le plan)

Terrain (contenance)	1 746 m²
Emprise bâtie	659 m² · 38 %
SDP du scénario (R+1)	1 176 m²
Stationnement + allée	0 m²
Pleine terre	970 m²
Places dessinées / imposées	30 / 30
Logements	30 · T1 ×24 · T2 ×6

LABUSE

Étude de faisabilité — plan masse

L'Étang-Salé · zone UA

Parcelles AW 99, 451, 624, 625

Scénario retenu · barre R+1 · stationnement aérien

PLU millésime en vigueur · LiDAR HD IGN · BD TOPO

Généré le 23/10/2026 · EF-23102026-8473


Esquisse indicative — pas une étude d'architecte

Planche — plan masse « façon architecte », dessinée depuis la géométrie du scénario (contexte : cadastre et bâti voisins BD TOPO, voies nommées, TN LiDAR aux angles). Esquisse indicative — pas une étude d'architecte.

5. Distribution et coupe

R+1 : la répartition des logements par niveau, chaque module dessiné = un logement compté.

Niveau	T1	T2	SDP du scénario
R+1	12	3	588
RDC	12	3	588
Total	24	6	1 176

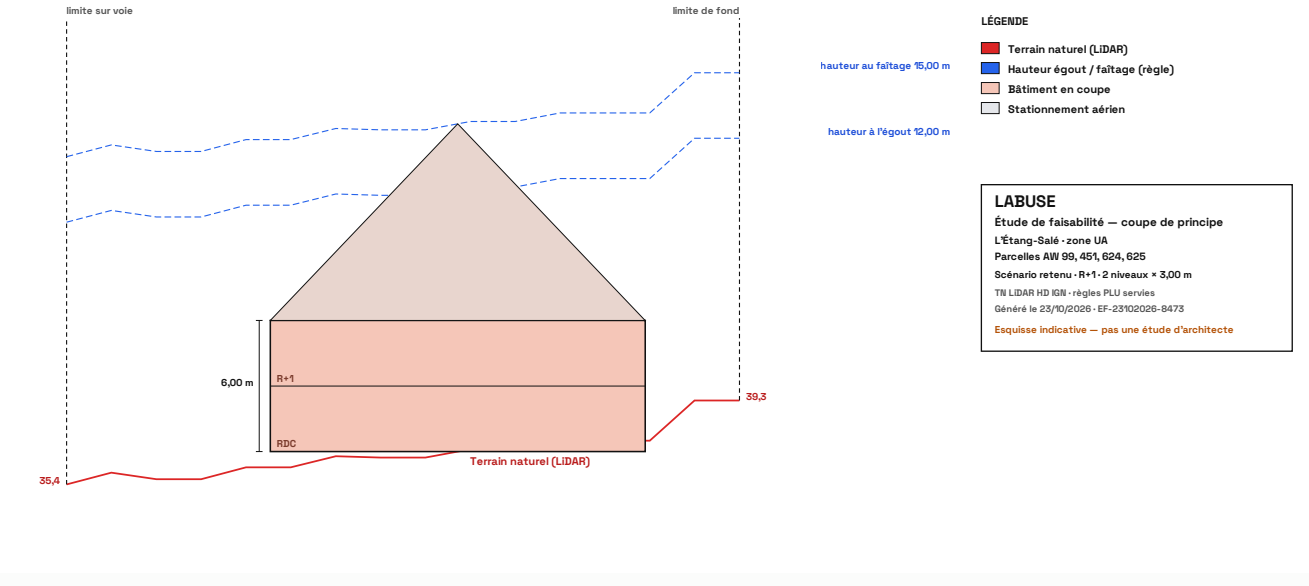

Coupe de principe : le volume bâti sous la règle de hauteur, le terrain naturel (LiDAR), le stationnement aérien au sol. Esquisse indicative, pas une étude d'architecte.

6. Capacité et contrôles

Scénario retenu : 9 contrôles réussis, 0 échoués, 1 non effectués. Ce n'est pas une validation réglementaire.

Programme	Nombre	Surface moy.	SHAB estimée	Nature
T1	24	30 m²	576 m²	Estimé
T2	6	56 m²	269 m²	Estimé
Dont logements aidés	6	quota PLU appliqué au programme		Sourcé

Programme saisi par le client (ses lignes T1–T4).

Contrôle	Règle	Scénario	Résultat

Emprise au sol PLU art. UA 2.4 · p. 18 — « Le pourcentage maximal de l'emprise au sol cumulée de l'ensemble des constructions est fixé à 70%. »	≤ 1222 m² (70 % de la contenance)	659 m²	Réussi
Hauteur PLU art. UA 2.5.2 · p. 19 — « La hauteur maximale des constructions est limitée à: - 12,00m à l'égout du toit - 15,00 m au faîtage - 13,00m à l'acrotère en cas de toiture-terrasse. »	≤ 12 m à l'égout	R+1 ≈ 6 m	Réussi
Hauteur sur terrain en pente La hauteur maximale des constructions est limitée à: - 12,00m à l'égout du toit - 15,00 m au faîtage - 13,00m à l'acrotère en cas de toiture-terrasse.	≤ 12 m à l'égout (toiture plate tenable)	R+1, relief sous bâti 4.1 m (RGE ALTI 5 m (IGN)) → 10.1 m aval	Réussi
Prospect (hauteur relative)	pas de règle de prospect	—	Non applicable
Reculs PLU art. UA 2.1 · p. 17 — « Les constructions doivent s'implanter en retrait de l'alignement, avec un recul minimum de 4,00 m par rapport à l'alignement. » ; PLU art. UA 2.2 · p. 17 — « Si une construction est implantée en retrait des limites séparatives d'une unité foncière, la marge d'isolement minimale doit être de 3,00m. »	voie 4 m · séparatives 3 m	bâti dans la zone d'implantation	Réussi
Perméabilité (pleine terre) PLU art. UA 2.6 · p. 21 — « Au moins 30% de la surface de la parcelle doit être perméable. »	≥ 524 m² (30 % de la contenance)	970 m²	Réussi
Espaces verts PLU art. UA 2.6 · p. 21 — « Les espaces verts (engazonnés) représentent au moins 20 % de la superficie du terrain, hors aires de stationnement ; 1 arbre pour 50 m² d'espaces verts. »	≥ 349 m² (20 % · hors stationnement)	1061 m²	Réussi
Marge plantée PLU art. UA 2.6 · p. 21 — « Une marge plantée de 2,00 m est aménagée sur au moins 75 % du linéaire des limites de l'unité foncière, hors limites mitoyennes. »	bande 2.0 m sur 75 % du linéaire hors mitoyenneté	reculs ≥ 3 m	Réussi
Stationnement PLU art. UA 2.7.3 · p. 22 — « Logement individuel Par logement 2 / Logement collectif 1 et 2 pièces 1 / 3 et 4 pièces 1,5 / 5 pièces et plus 2 »	≥ 30 places (barème validé)	30 places au sous-sol	Réussi
Emprise du sous-sol PLU art. UA 2.4 · p. 18 — « Le pourcentage maximal de l'emprise au sol cumulée de l'ensemble des constructions est fixé à 70%. »	≤ 1222 m² (emprise réglementaire, CES 70 %)	750 m² (30 places × 25 m²)	Réussi
Distance entre constructions	sans objet (un seul bâtiment)	un seul bâtiment	Non applicable
Locaux vélos · déchets	non modélisés	—	Non effectué
PPR zone rouge (interdiction)	absente du terrain	—	Non applicable

PPR zone bleue (prescription)	absente du terrain	—	Non applicable
ER / EBC / SUP / servitudes	absentes du terrain	—	Non applicable

Un contrôle « Échoué » retire le scénario des « Exploitable ». « Non effectué » ne vaut jamais « Réussi ».

7. Hypothèses, limites, sources

Ce que l'étude suppose, ce qu'elle ne sait pas, d'où viennent les chiffres.

Hypothèses (toutes « Estimé », modifiables dans l'outil)

Hypothèse	Valeur	Convention
Profondeur de bâtiment	13 m	logements traversants, coursive extérieure
Surface moyenne par type	30 / 56 / 65 / 80 m²	modifiable
Plancher → habitable	0,8	circulations et noyaux hors habitable
Place · allée	2,5 × 5 m · allée 5 m	dimensions usuelles
Hauteur de niveau	3 m	convention
Stationnement	sous-sol 1 niveau	aérien (au sol) ou sous-sol (niveaux choisis : -1, ou -1 et -2)

À faire confirmer par l'architecte

Point	Pourquoi
Distance entre constructions · locaux vélos et déchets	règles non modélisées
Prescriptions PPR bleue · servitudes signalées	signalées, non interprétées
Accès véhicule	limite classée voie ; visibilité et autorisation non vérifiées
Sol, réseaux, arbres, vues, voisinage	aucune donnée publique fiable à la parcelle
Conception (plans, façades)	métier de l'architecte

Sources

Source	Nature
PLU — zone UA	règlement, zonage, prescriptions publiés

Cadastre DGFiP · PPR, servitudes (GPU, Géorisques)	**données publiques**
LiDAR HD IGN · BD TOPO	**terrain naturel, limites**
Moteur d'implantation LABUSE	**hypothèses « Estimé », modifiables dans l'outil**

Entrées, configuration, version du moteur et des règles archivées avec le document n° EF-f36c0b32 : le scénario se rejoue à l'identique.

Annexe — extraits du règlement

PLU de L'Étang-Salé · zone UA · millésime 2025-09-17. Chaque règle appliquée est citée mot pour mot.

recul sur voie — art. UA 2.1 · p. 17 · millésime 2025-09-17
« Les constructions doivent s'implanter en retrait de l'alignement, avec un recul minimum de 4,00 m par rapport à l'alignement. »

recul sur limites séparatives — art. UA 2.2 · p. 17 · millésime 2025-09-17
« Si une construction est implantée en retrait des limites séparatives d'une unité foncière, la marge d'isolement minimale doit être de 3,00m. »

emprise au sol (CES) — art. UA 2.4 · p. 18 · millésime 2025-09-17
« Le pourcentage maximal de l'emprise au sol cumulée de l'ensemble des constructions est fixé à 70%. »

hauteur à l'égout — art. UA 2.5.2 · p. 19 · millésime 2025-09-17
« La hauteur maximale des constructions est limitée à: - 12,00m à l'égout du toit - 15,00 m au faîtage - 13,00m à l'acrotère en cas de toiture-terrasse. »

hauteur au faîtage — art. UA 2.5.2 · p. 19 · millésime 2025-09-17
« La hauteur maximale des constructions est limitée à: - 12,00m à l'égout du toit - 15,00 m au faîtage - 13,00m à l'acrotère en cas de toiture-terrasse. »

pleine terre (perméabilité) — art. UA 2.6 · p. 21 · millésime 2025-09-17
« Au moins 30% de la surface de la parcelle doit être perméable. »

mixité sociale — art. UA 1.3 (1) · p. 17 · millésime 2025-09-17
« « Tout projet visant à créer plus de 1 000 m² de surface de plancher destinée à l'habitation doit prévoir d'affecter au logement aidé au moins 20% de la surface de plancher d'habitation prévue dans l'opération. » »

stationnement (barème) — art. UA 2.7.3 · p. 22 · millésime 2025-09-17
« Logement individuel Par logement 2 / Logement collectif 1 et 2 pièces 1 / 3 et 4 pièces 1,5 / 5 pièces et plus 2 »

Document PLU officiel : `https://data.geopf.fr/telechargement/download/pack_plu1/PACK_DU_97404_0f997d78ccf283bce6b463fd84eeb274/97404_PLU_20250917.zip`